क्षेत्रीय रेल प्रशिक्षण संस्थान, भूली

ZONAL RAILWAY TRAINING INSTITUTE, BHULI

STATION

Dhananjay Kumar Singh
Instructor
ZRTI, Bhuli

STATION

- "station" means any place on a line of railway at which traffic is dealt with, or at which an authority to proceed is given under the system is working.

STATION

STATION

BLOCK STATION

1. CLASS "A" STATION
2. CLASS "B" STATION
3. CLASS "C" STATION
4. SPL CLASS STATION

NON-BLOCK STATION

1. CLASS "D" STATION
2. CLASS DK" STATION

STATION

BLOCK STATION

- Block stations are those at which the Driver must obtain an authority to proceed under the system of working to enter the block section with his train.

STATION

NON BLOCK STATION


- Non-block stations are stopping places which are situated between two consecutive block stations, and do not form the boundary of any block section.

STATION

CLASS "A" STATION


- Class 'A' stations - where Line Clear may not be given for a train unless the line on which it is intended to receive the train is clear for at least 400 metres beyond the Home signal, or upto the Starter.

CLASS 'A' STATION

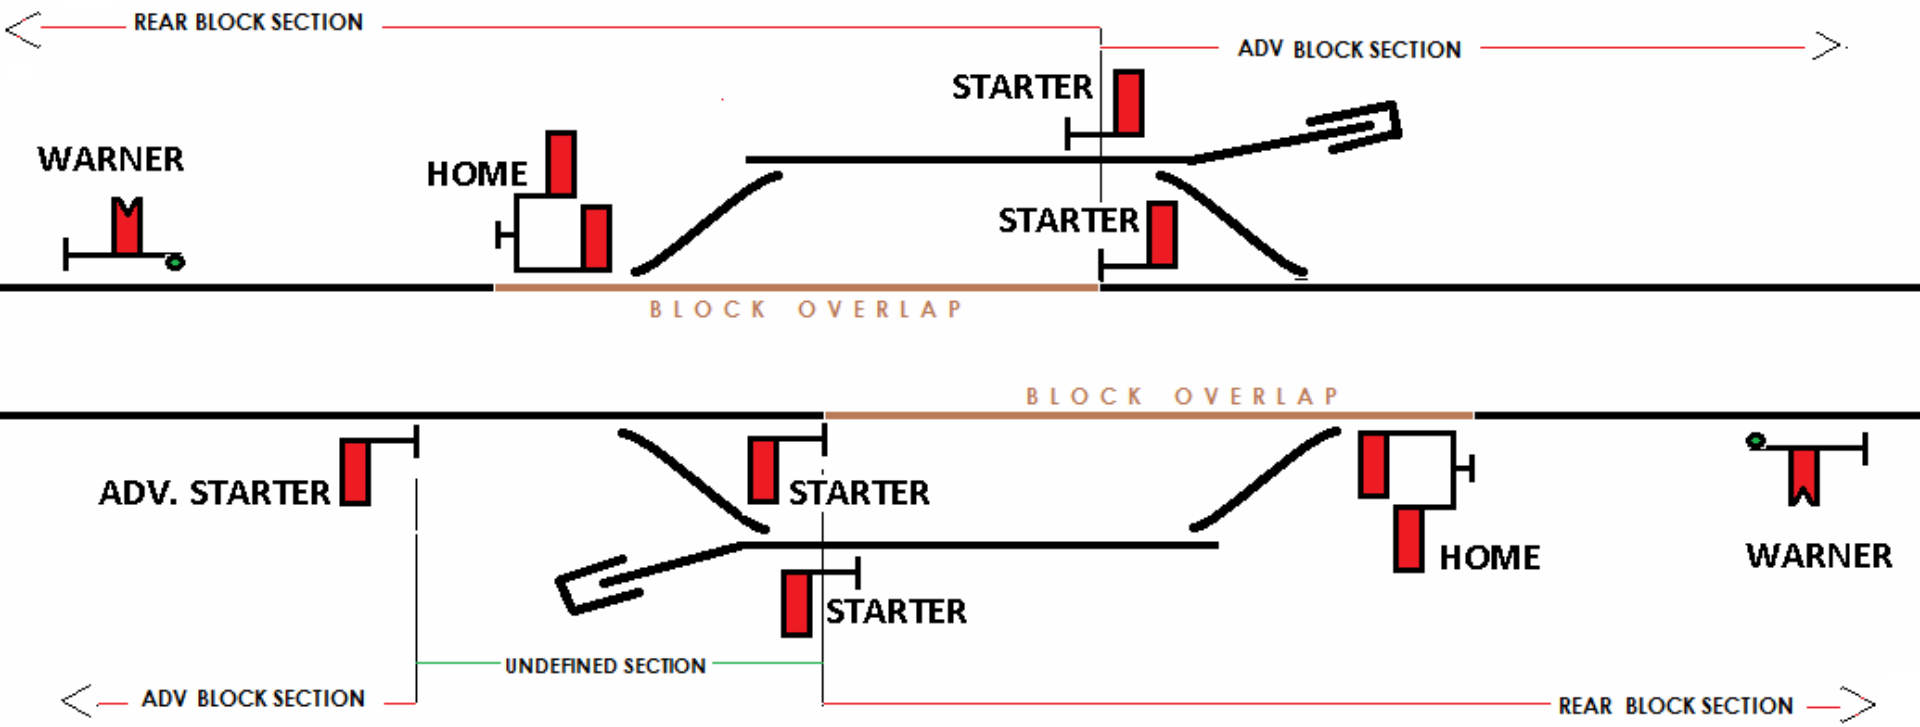


"A" CLASS STATION

CLASS 'A' STATION

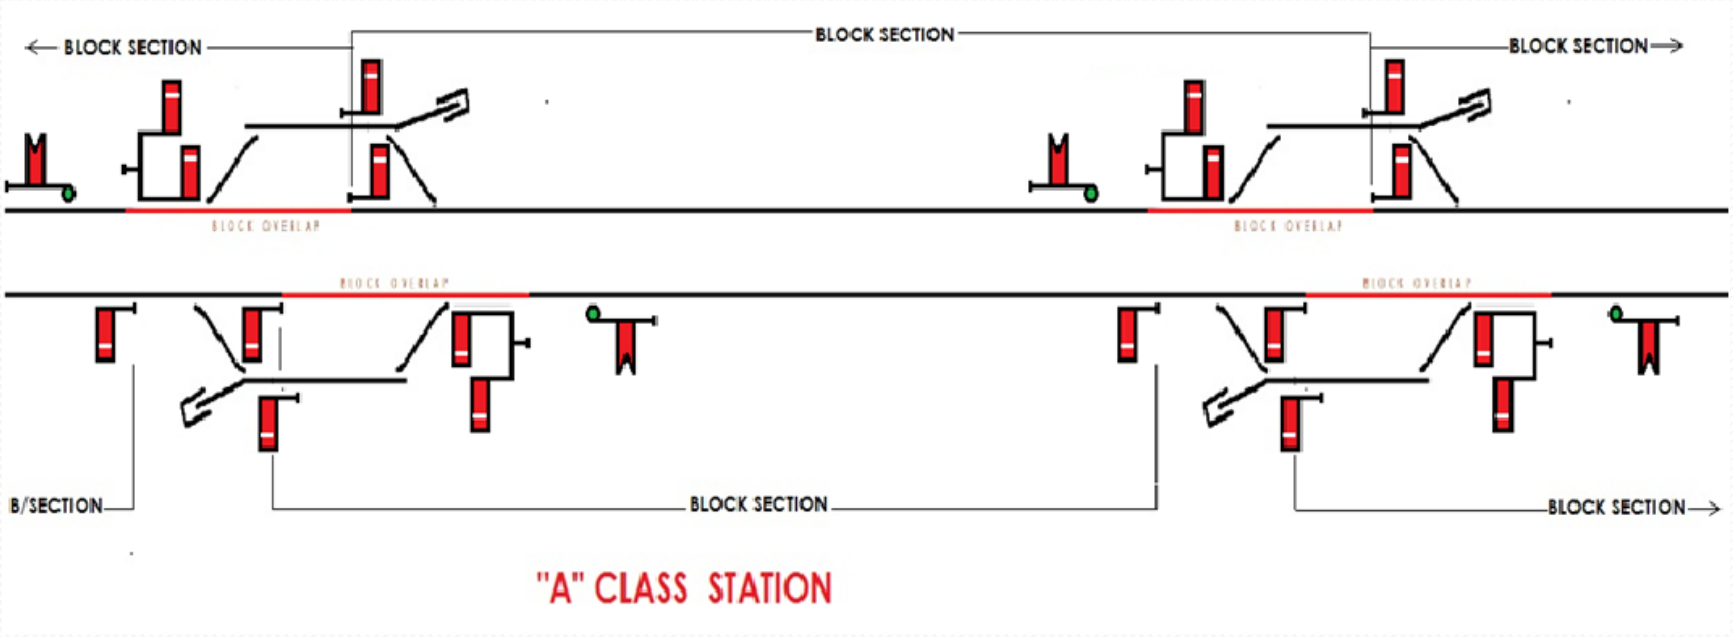


"A" CLASS STATION

NUMBER OF TRAINS BETWEEN TWO 'A' CLASS STATION

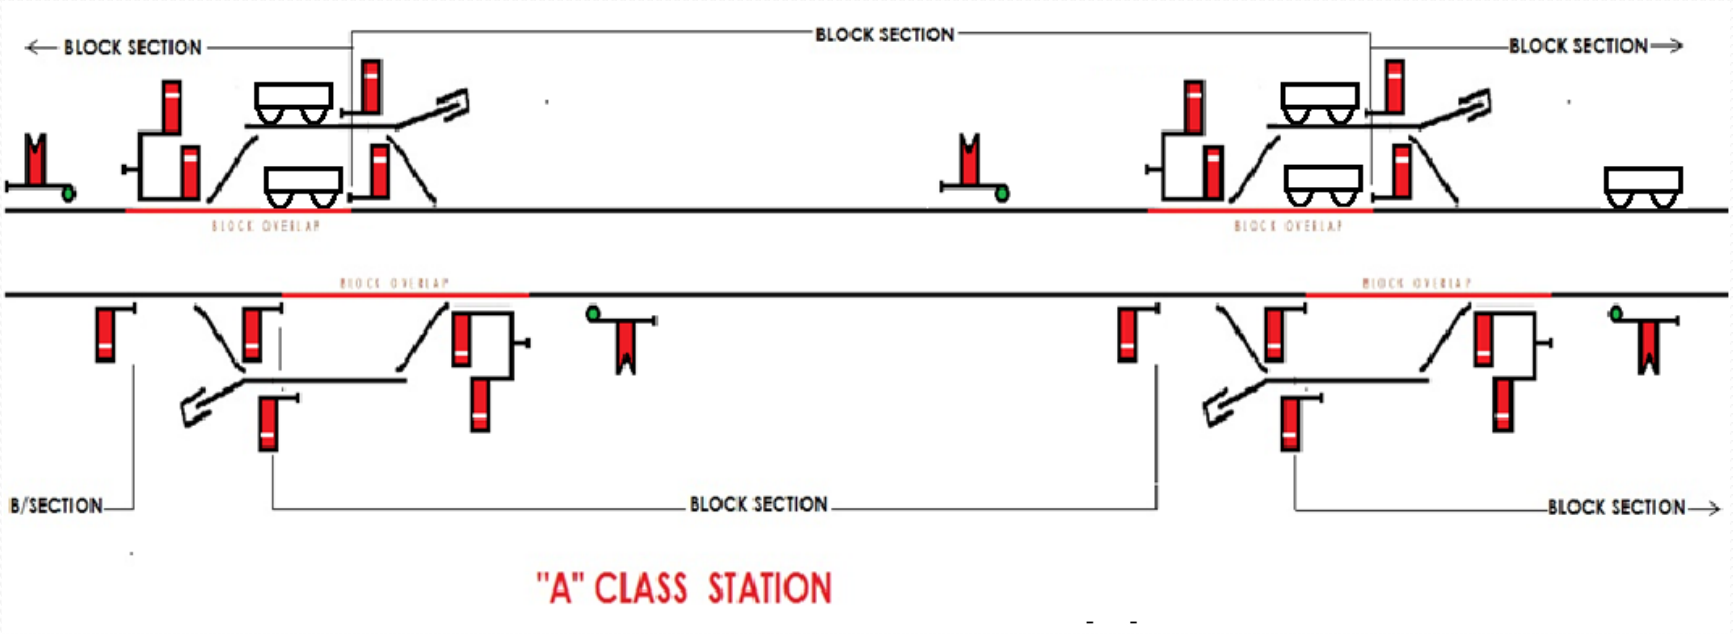

"A" CLASS STATION


NUMBER OF TRAINS BETWEEN TWO 'B' CLASS STATION

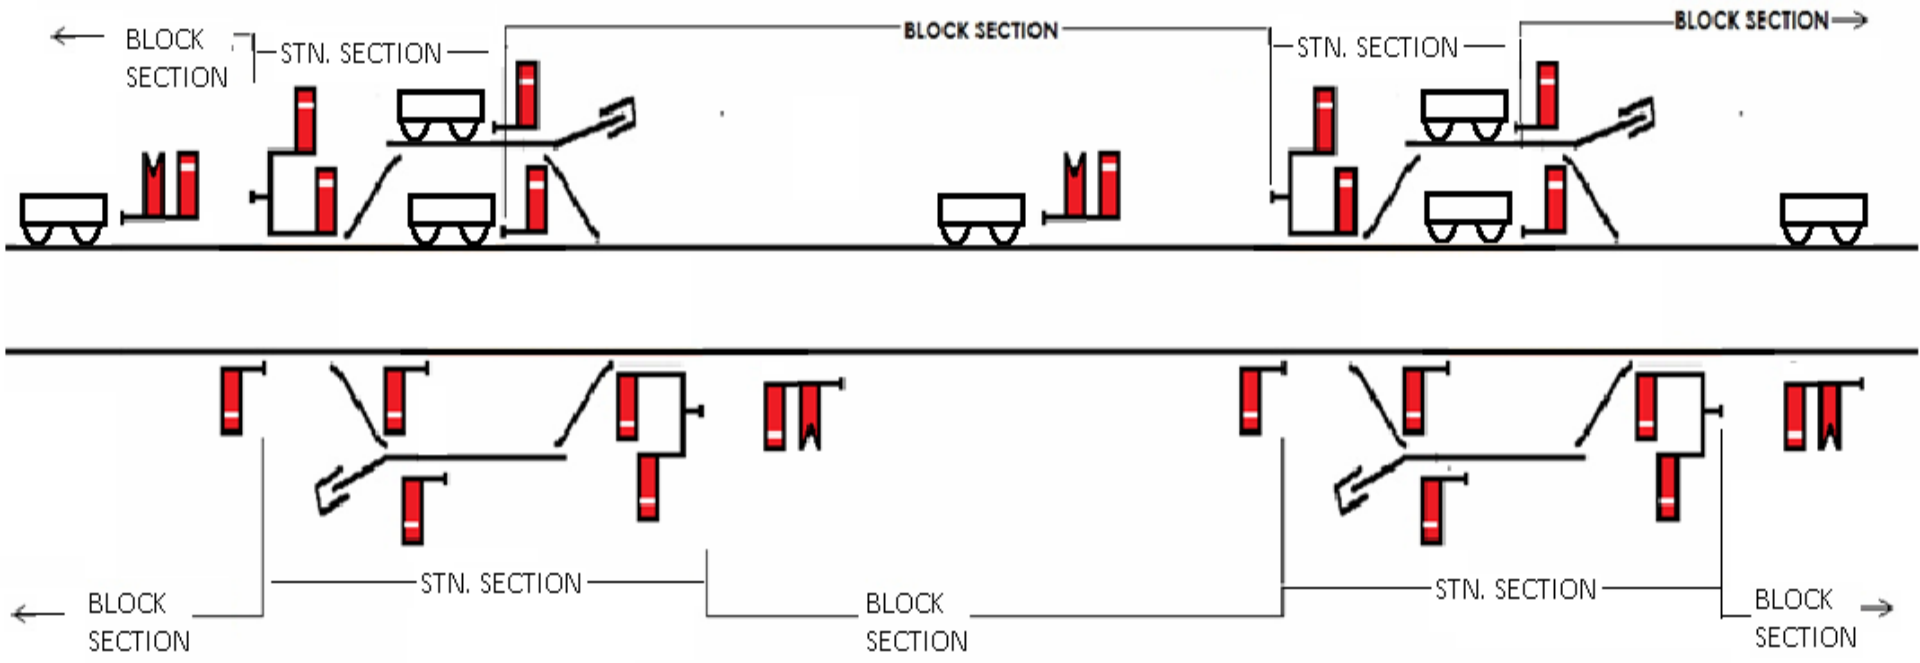


CLASS "B" STATION

- Class 'B' stations - where Line Clear may be given for a train before the line has been cleared for the reception of the train within the station section.

Class “B” Single line station in two-aspect signalling territory with Outer and Home signals

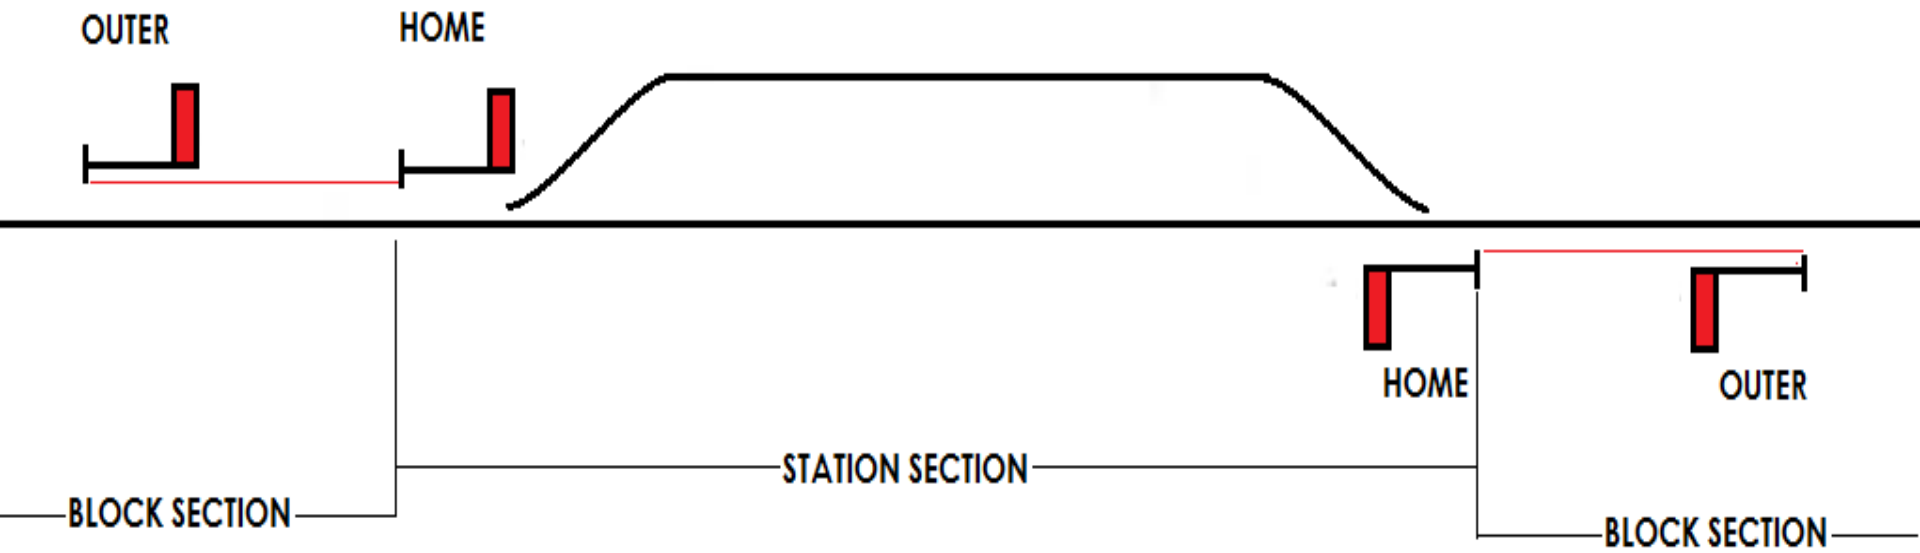


Class 'B' Single line station in two aspect signalling with Outer and Home signals (Note to Rule 8.03 refers)

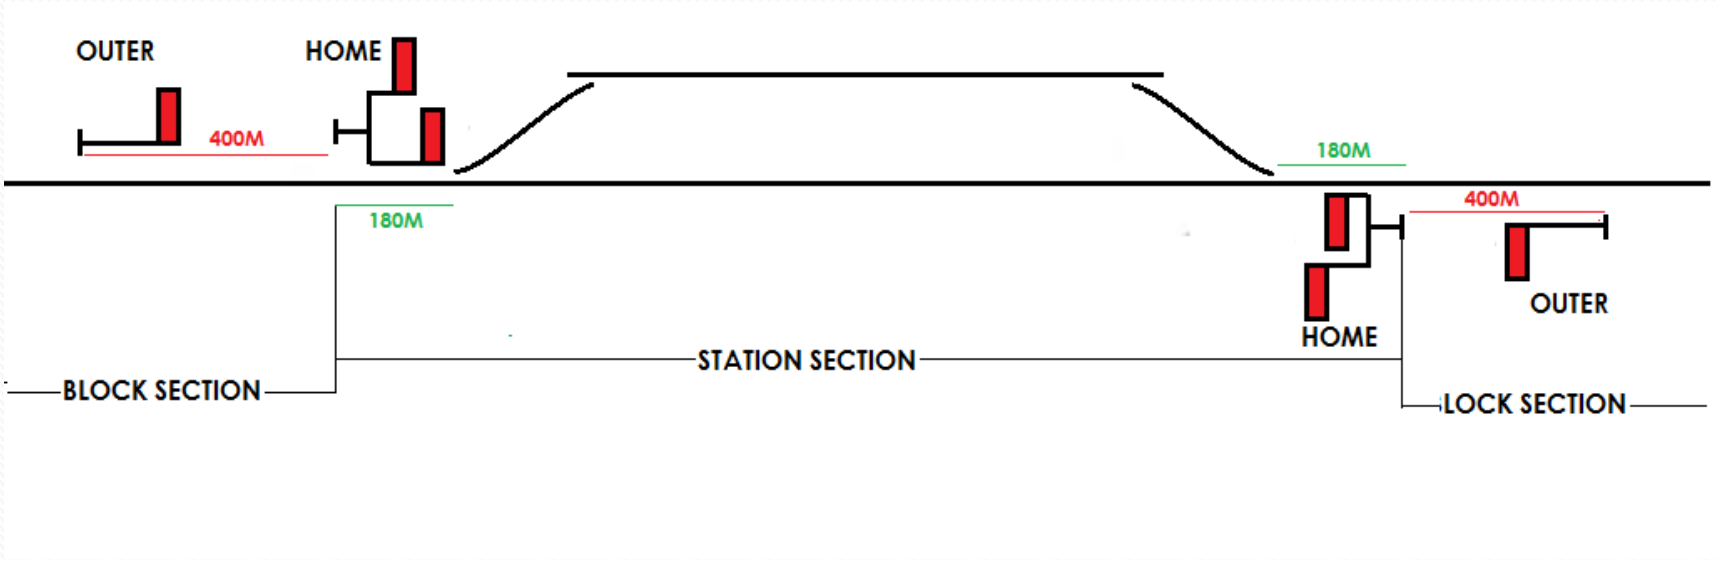


Note to Rule 8.03

- ***At a class 'B' single line station, this rule does not forbid direct reception of a train from one side, when Line Clear has been given to the block station on the other side provided the distance between the Outer signal and outermost facing points in two-aspect signalling, is not less than the sum-total of the adequate distances prescribed in Rule 8.01 in regard to conditions for granting Line Clear and Rule 3.40 in regard to conditions for taking 'off' Home signal for !he admission of a train even where Shunting Limit Boards or Advanced Starters have not been provided as prescribed in sub-rule (1) of Rule 3.32.`***


CLASS 'B' SINGLE LINE STATION IN TWO ASPECT SIGNALS WITH WARNER, OUTER, HOME, STARTER AND ADVANCED STARTER SIGNALS / SHUNTING LIMIT BOARDS

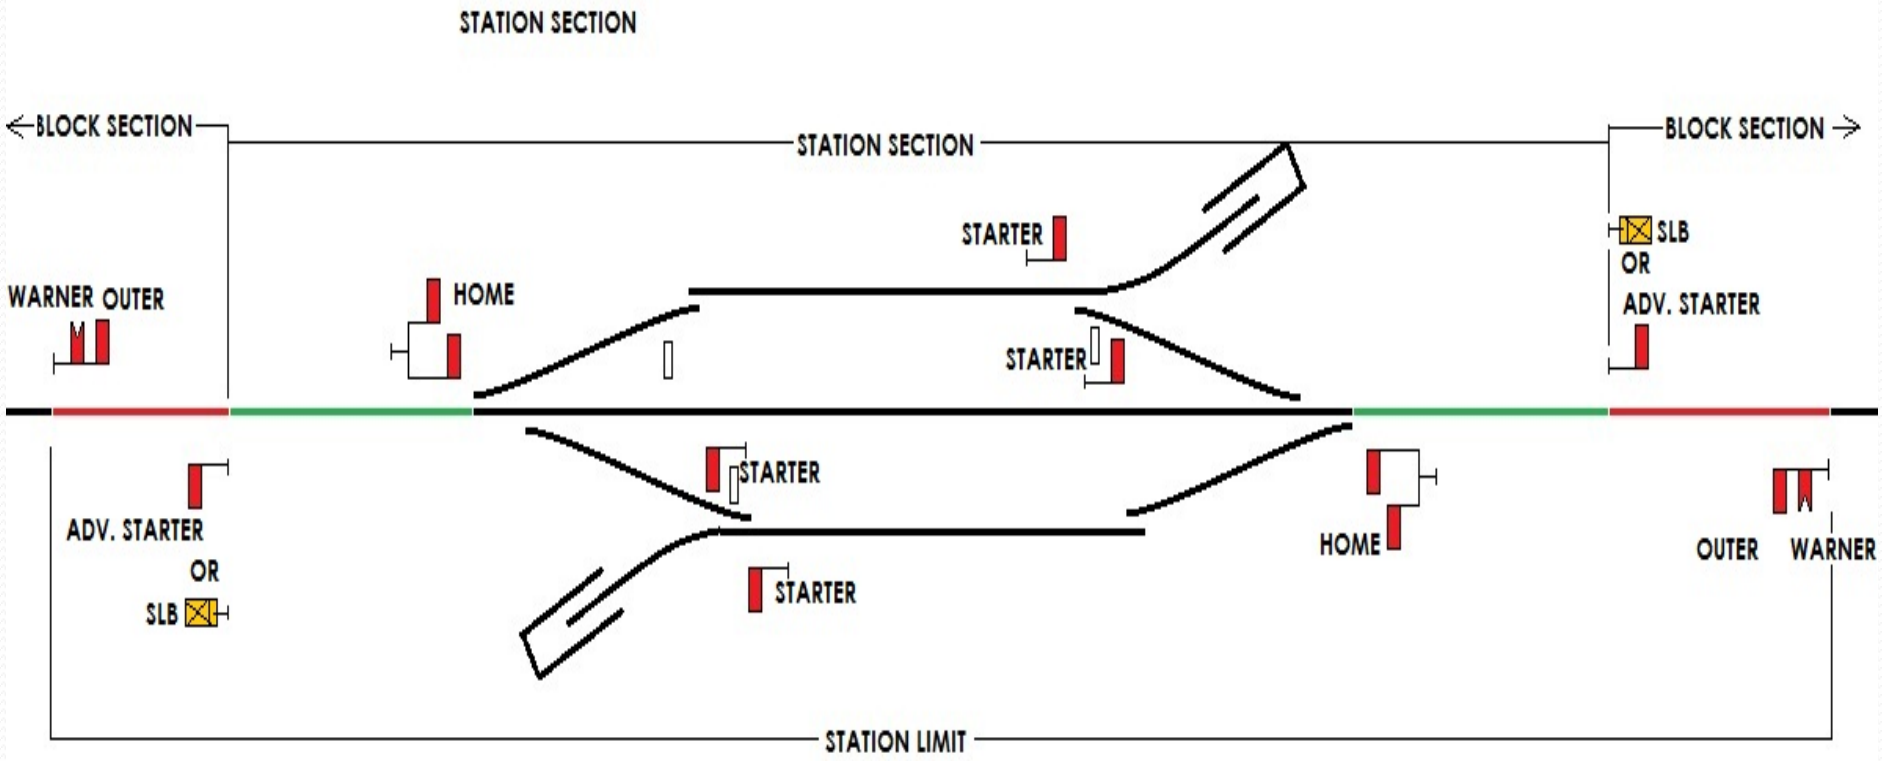

CLASS 'B' SINGLE LINE STATION IN TWO ASPECT SIGNAL WITH WARNER, OUTER, HOME, STARTER AND ADVANCED STARTER SIGNALS / SHUNTING LIMIT BOARDS

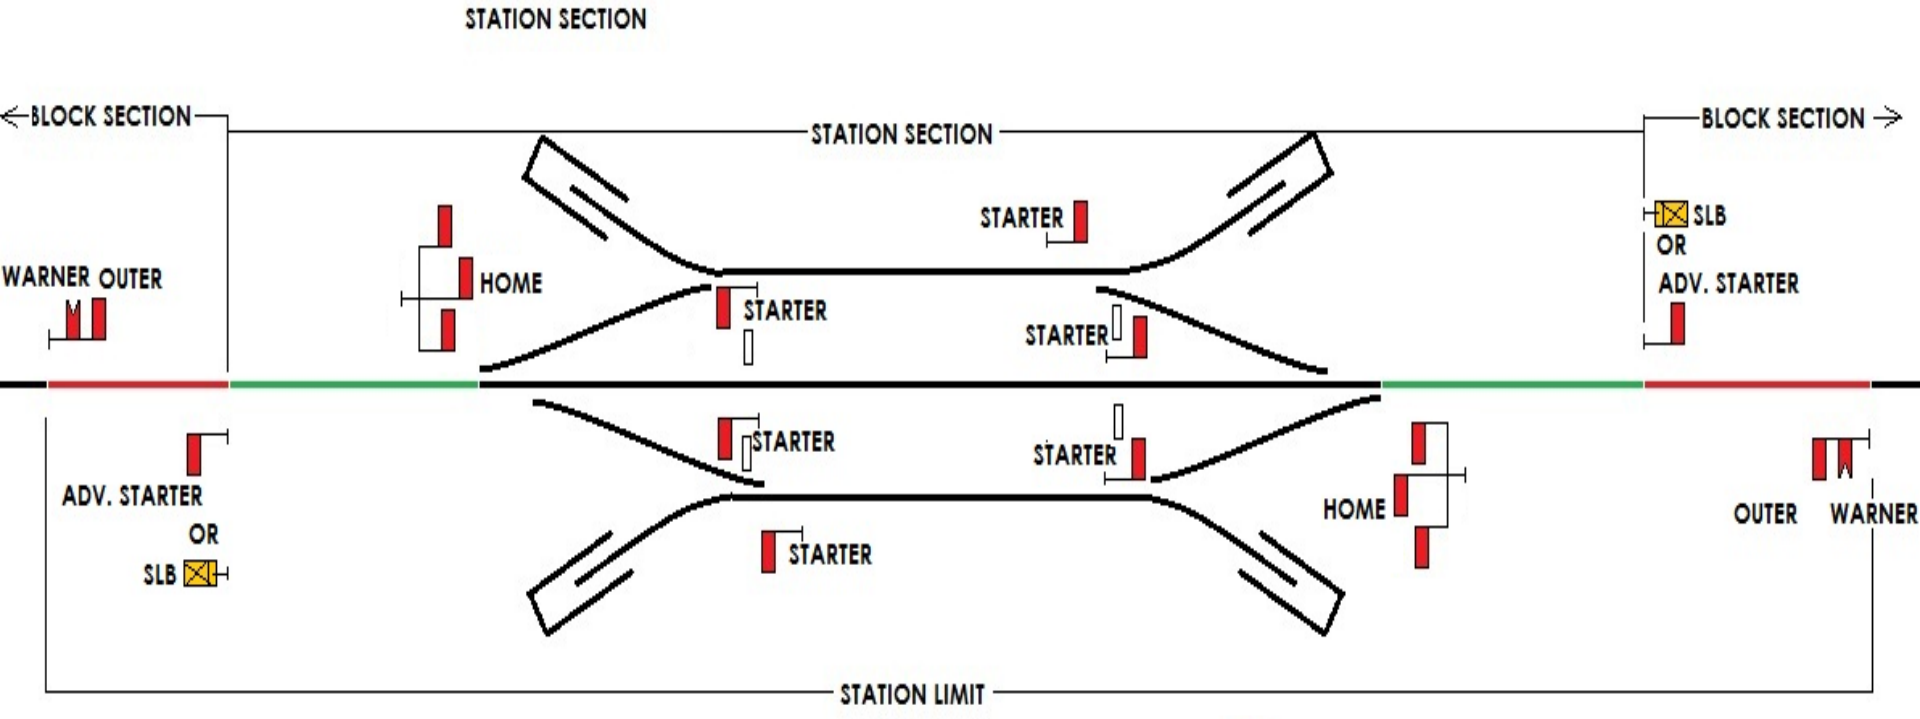

Class "B" Double line station in two-aspect signals with Warner,Outer, Home, Starter and Advanced Starter signals

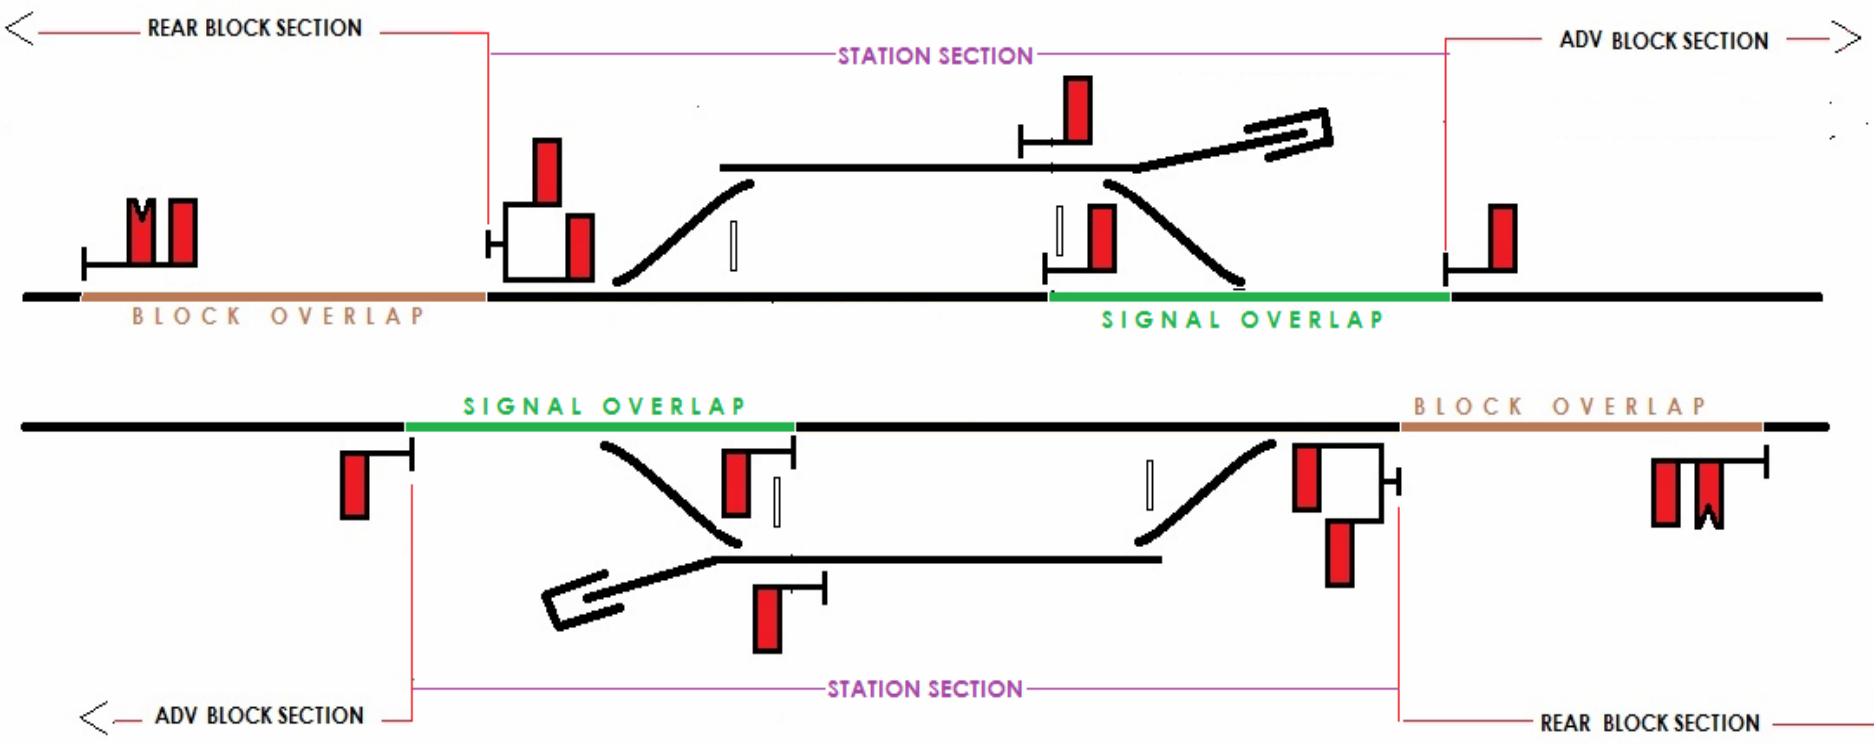


STATION SECTION


"B" CLASS STATION

D.K.SINGH/ Instructor/ZRTI / Bhuli

Class 'B' Single line station in multiple-aspect signals with Distant, Home, Starter, Adv. Starter / Shunting Limit Board

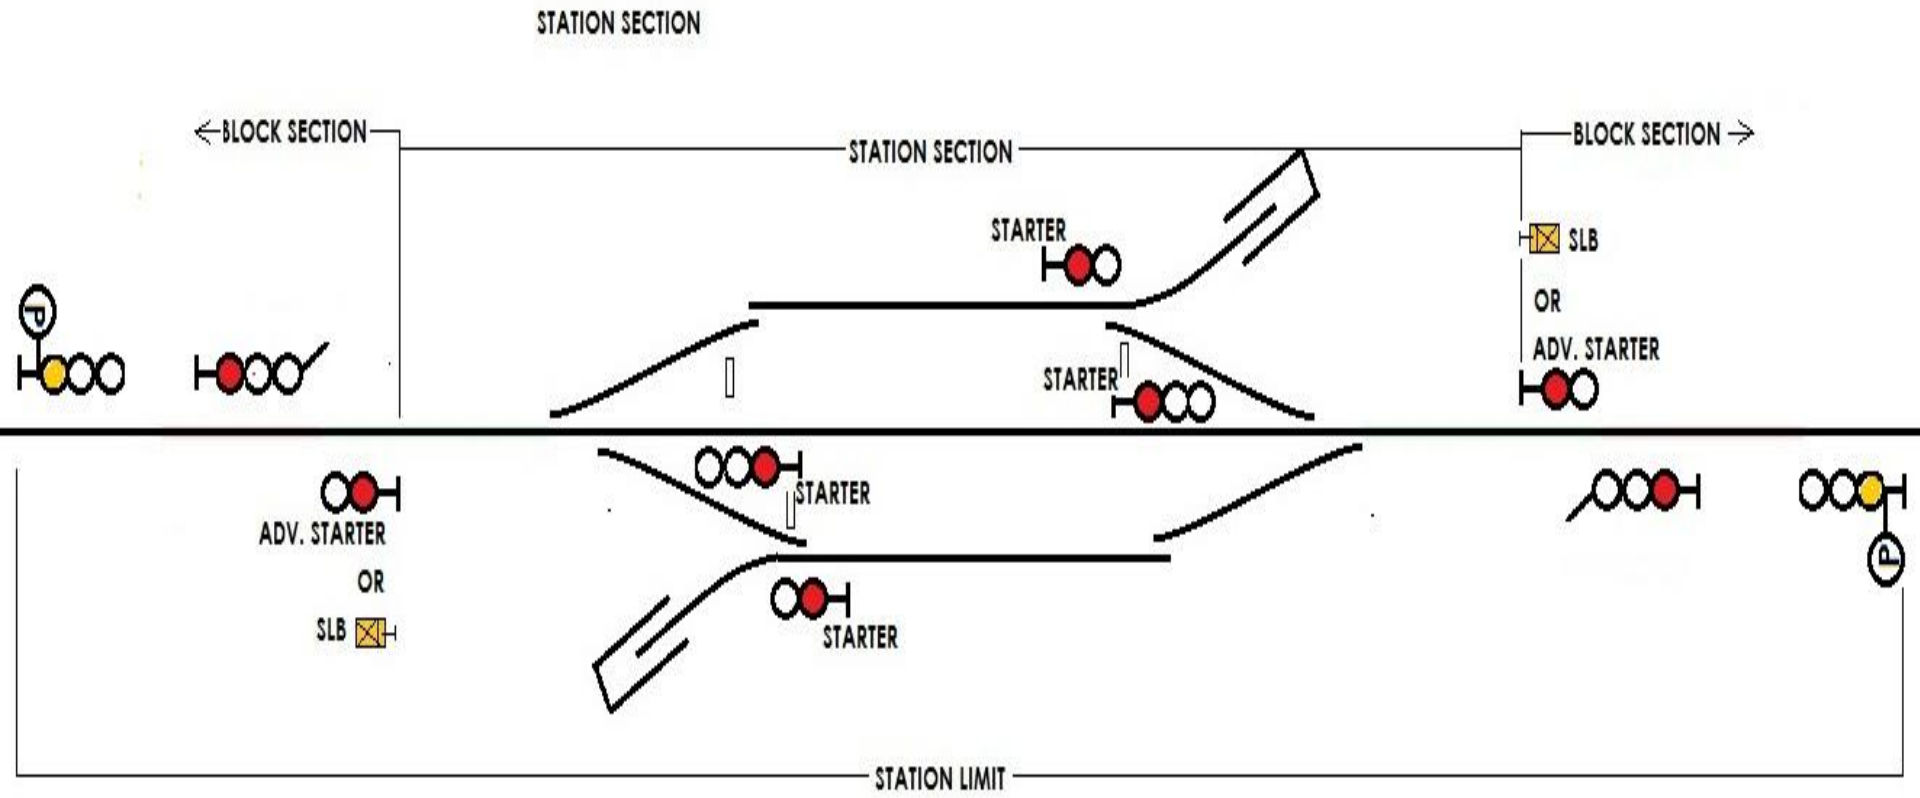


Class 'B' Double line station in multiple-aspect signals with Distant, Home, Starter, Advance Starter signals and Block Section Limit Board

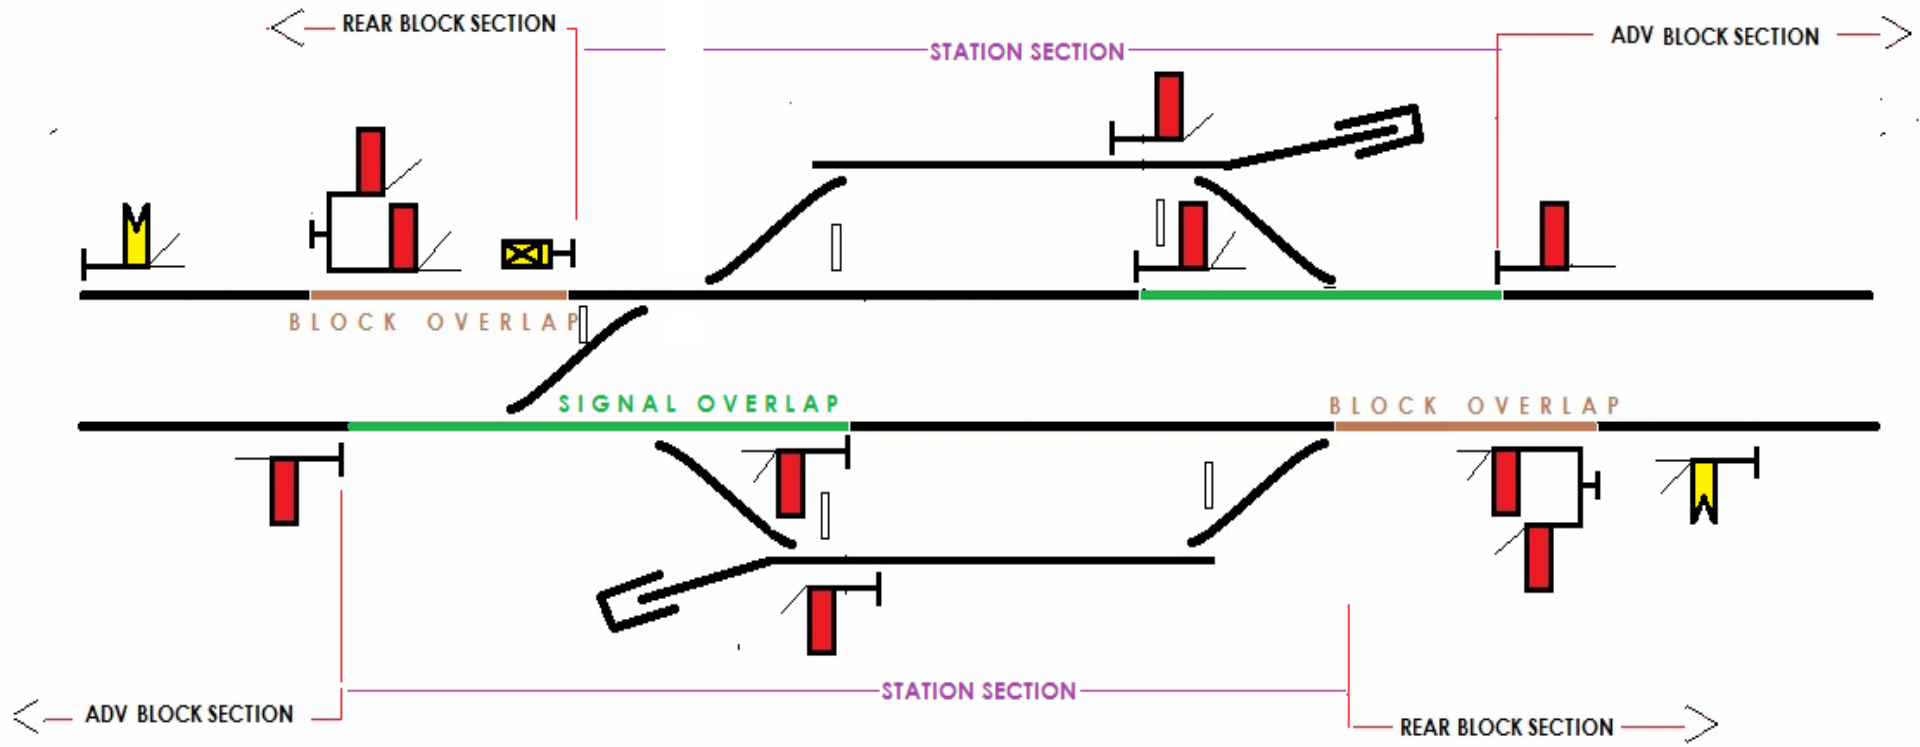

"B" CLASS STATION


D.K.SINGH/ Instructor/ZRTI / Bhuli

Class 'B' Double line station in multiple-aspect signals with Distant, Home, Starter, Advance Starter signals and Block Section Limit Board & Goods Shed

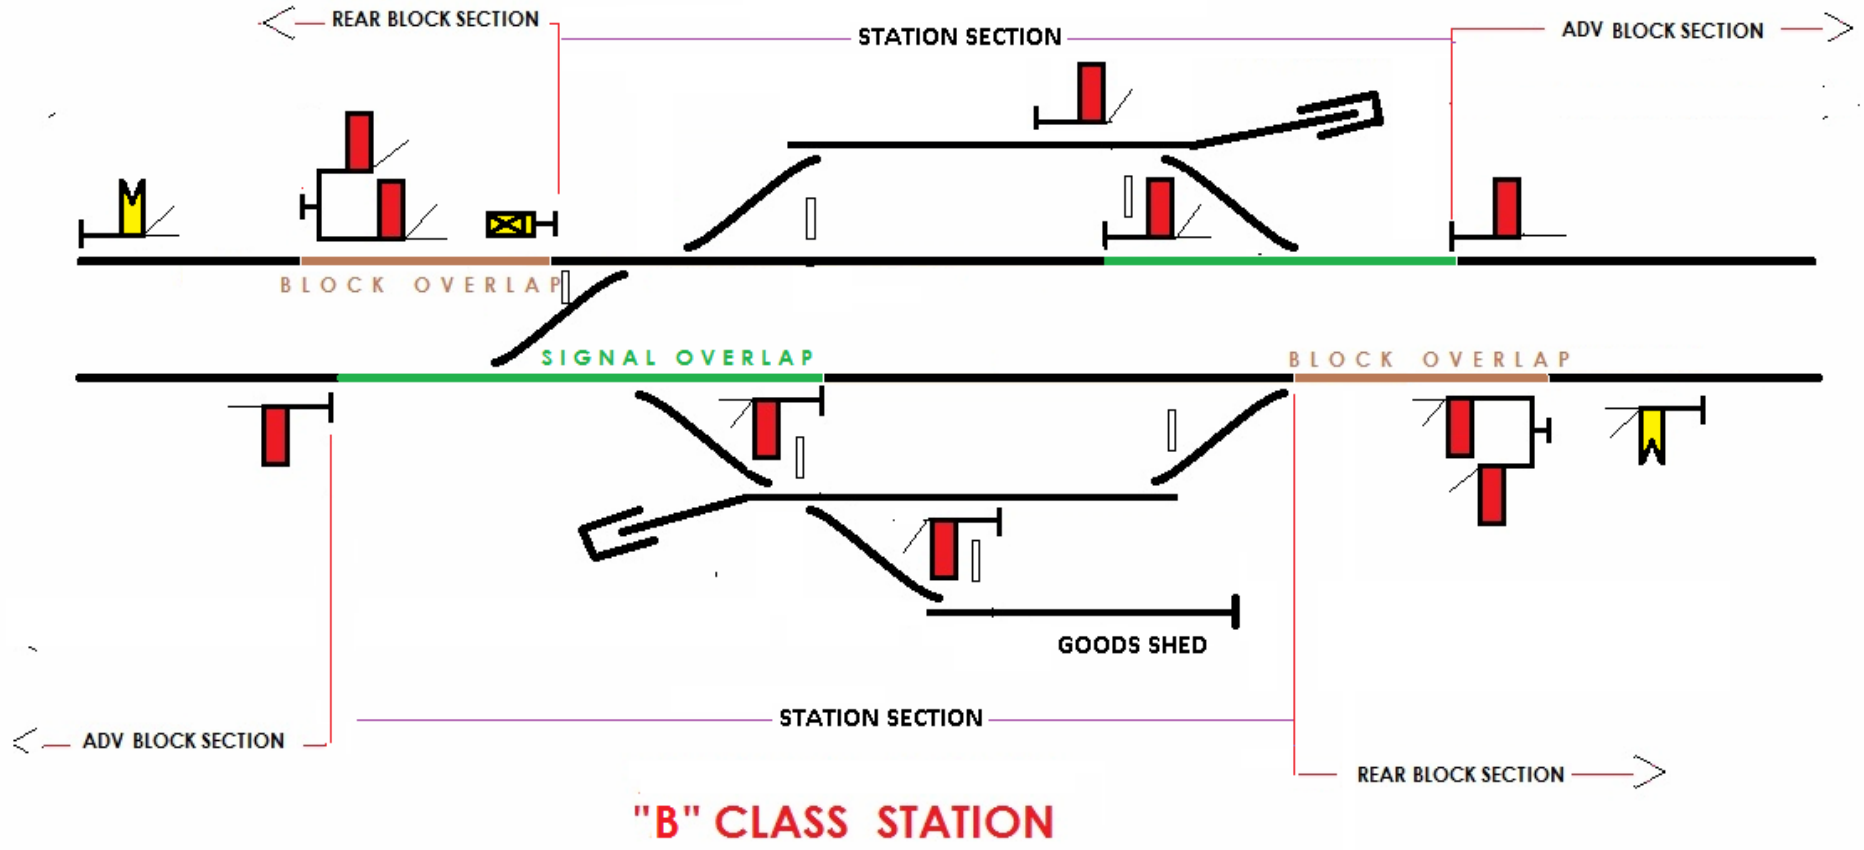

"B" CLASS STATION


Class 'B' Double line station in multiple-aspect signals with Distance, Home, Starter, Advance Starter signals and Block Section Limit Board

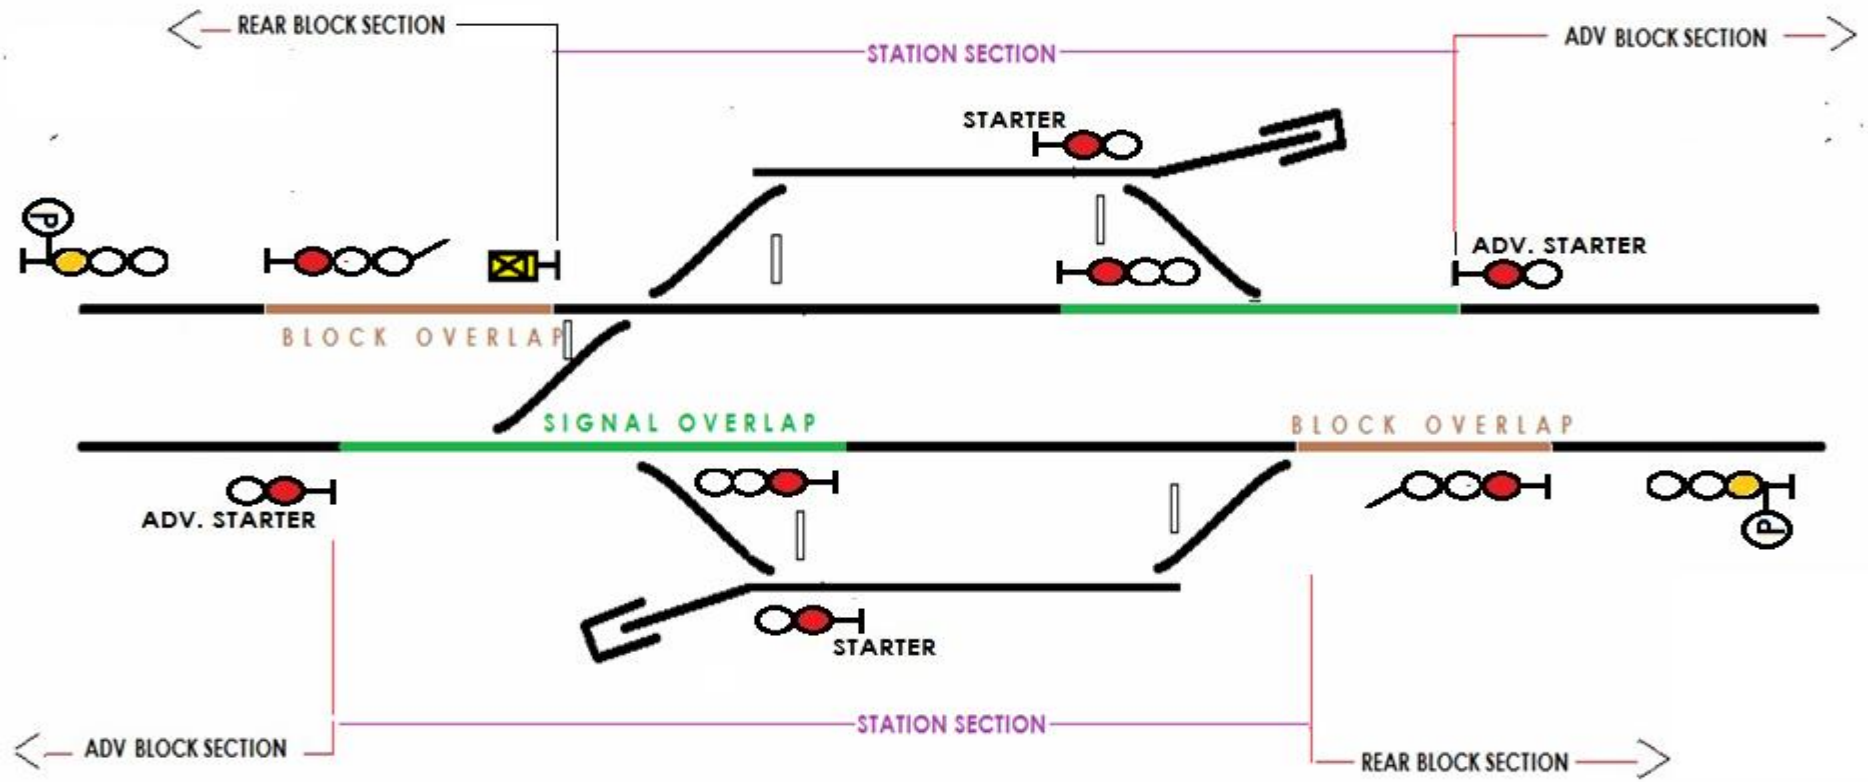

"B" CLASS STATION


D.K.SINGH/ Instructor/ZRTI / Bhuli

Class 'B' Double line station in multiple-aspect signals with Distant, Home, Starter, Advance Starter signals and Block Section Limit Board & Goods Shed

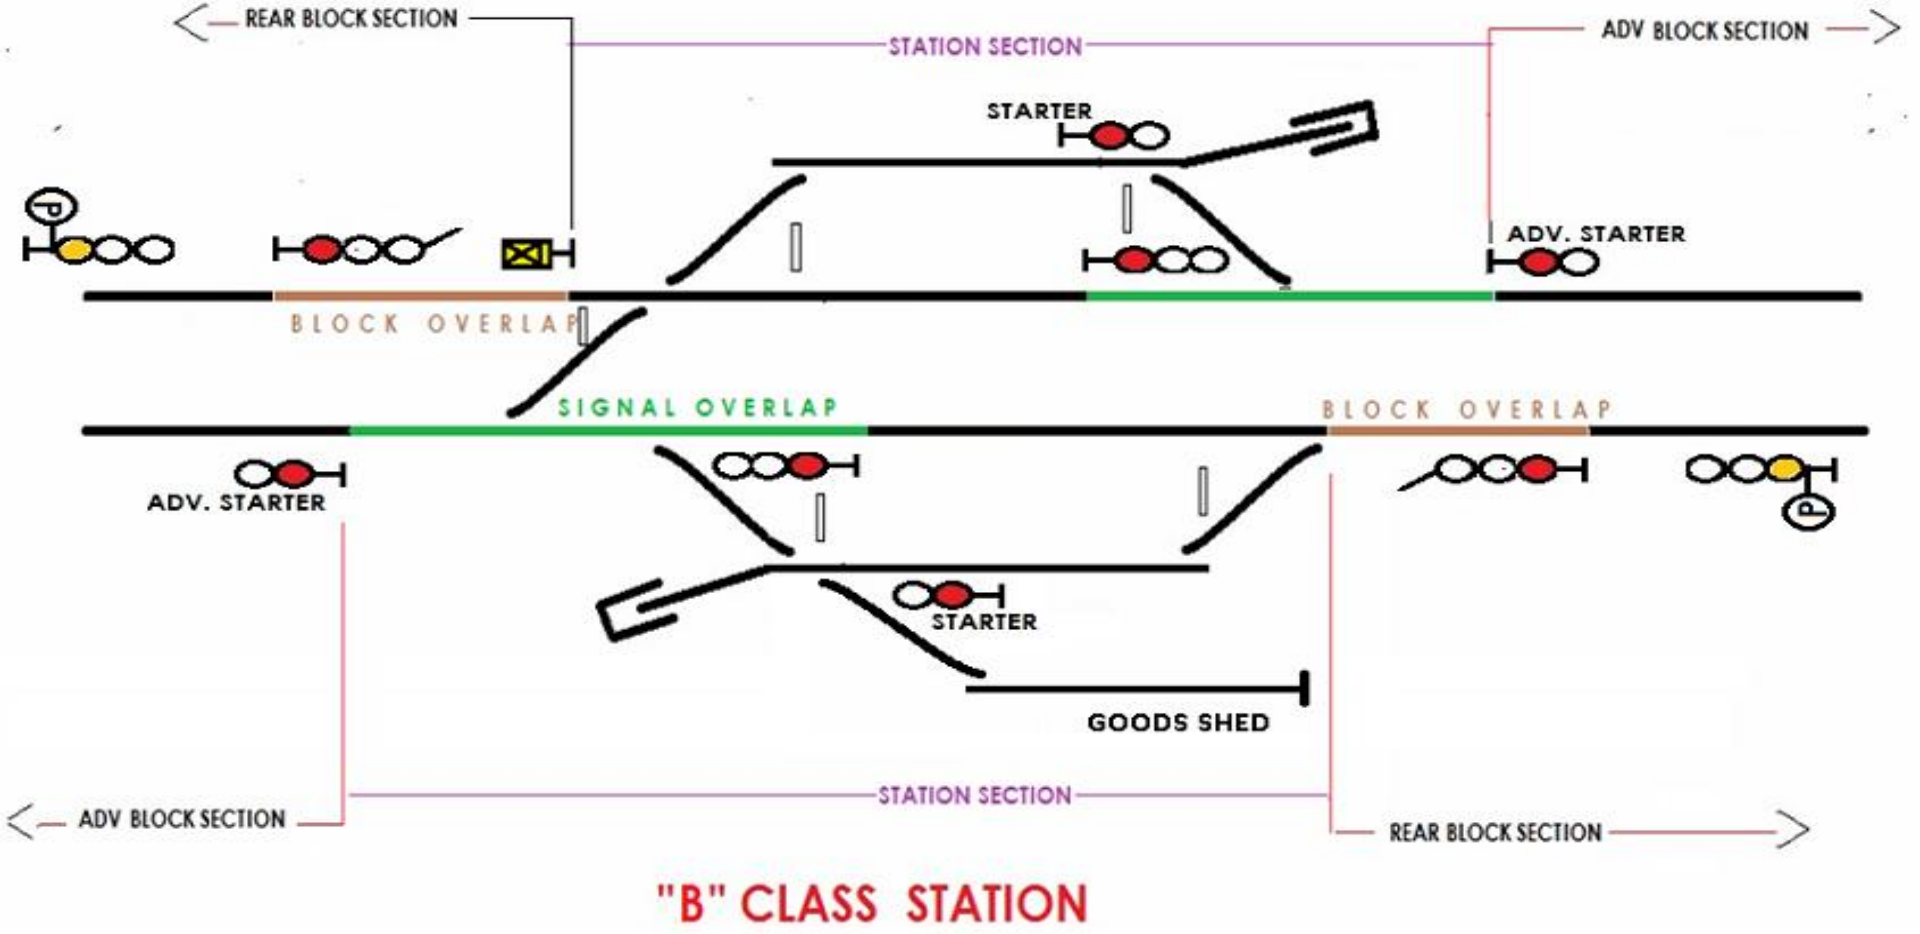


"B" CLASS STATION

Class 'B' Double line station in multiple-aspect signals with Double Distant, Home, Starter, Advance Starter signals and Block Section Limit Board & Goods Shed

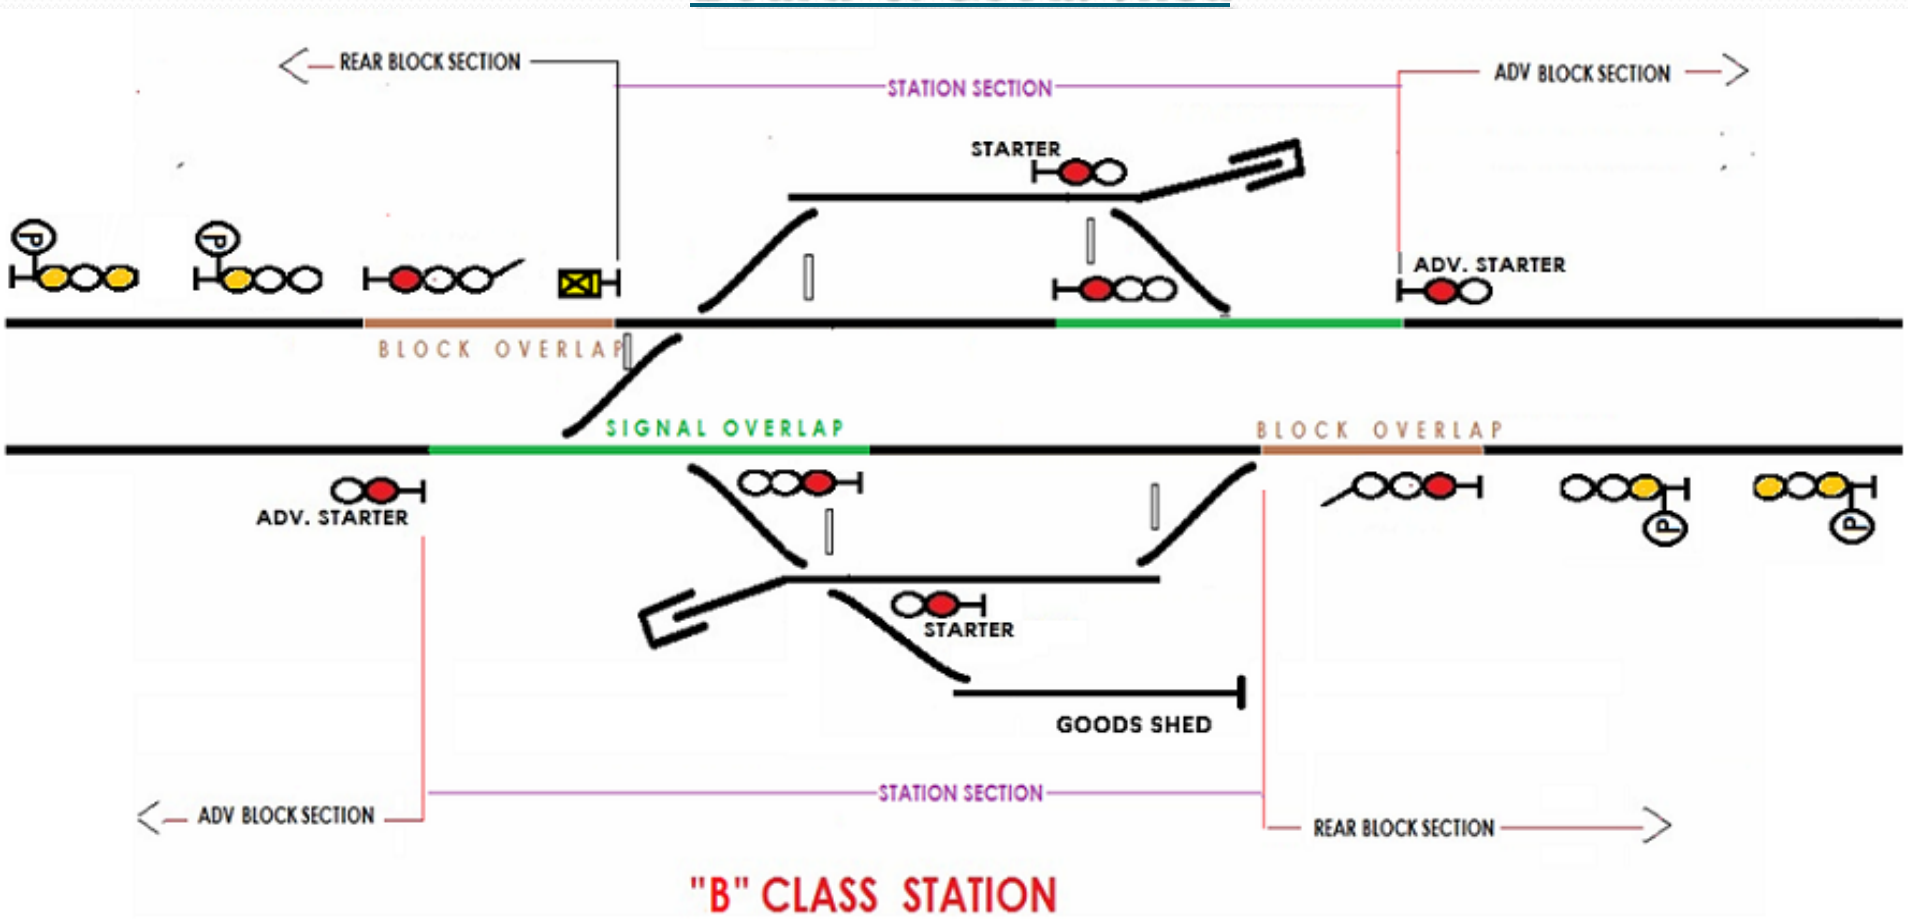


Class 'B' Double line station in multiple-aspect signals with Distant, Home, Starter signals and Block Section Limit Board

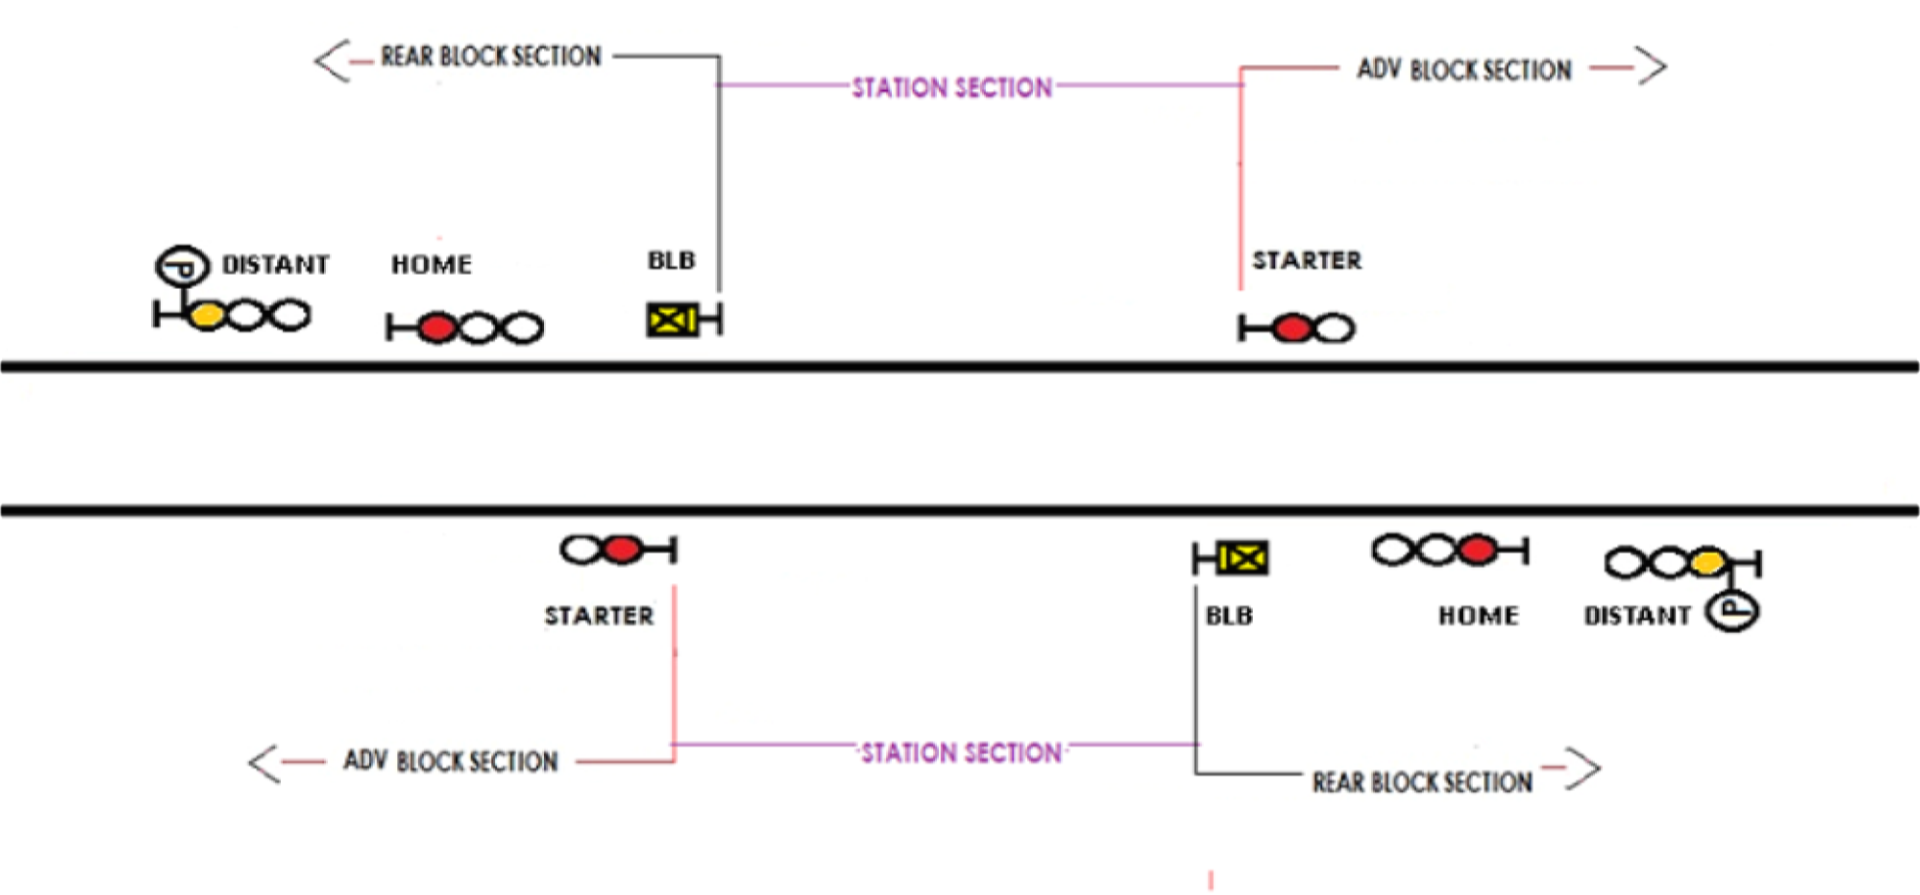


CLASS "C" STATION

- **Where line clear may not be given for a train, unless the whole of the last preceding train has passed complete at least 400 metres beyond the Home Signal and is continuing its journey.**


CLASS 'C' DOUBLE LINE STATION IN TWO ASPECT SIGNALS WITH WARNER AND HOME SIGNALS

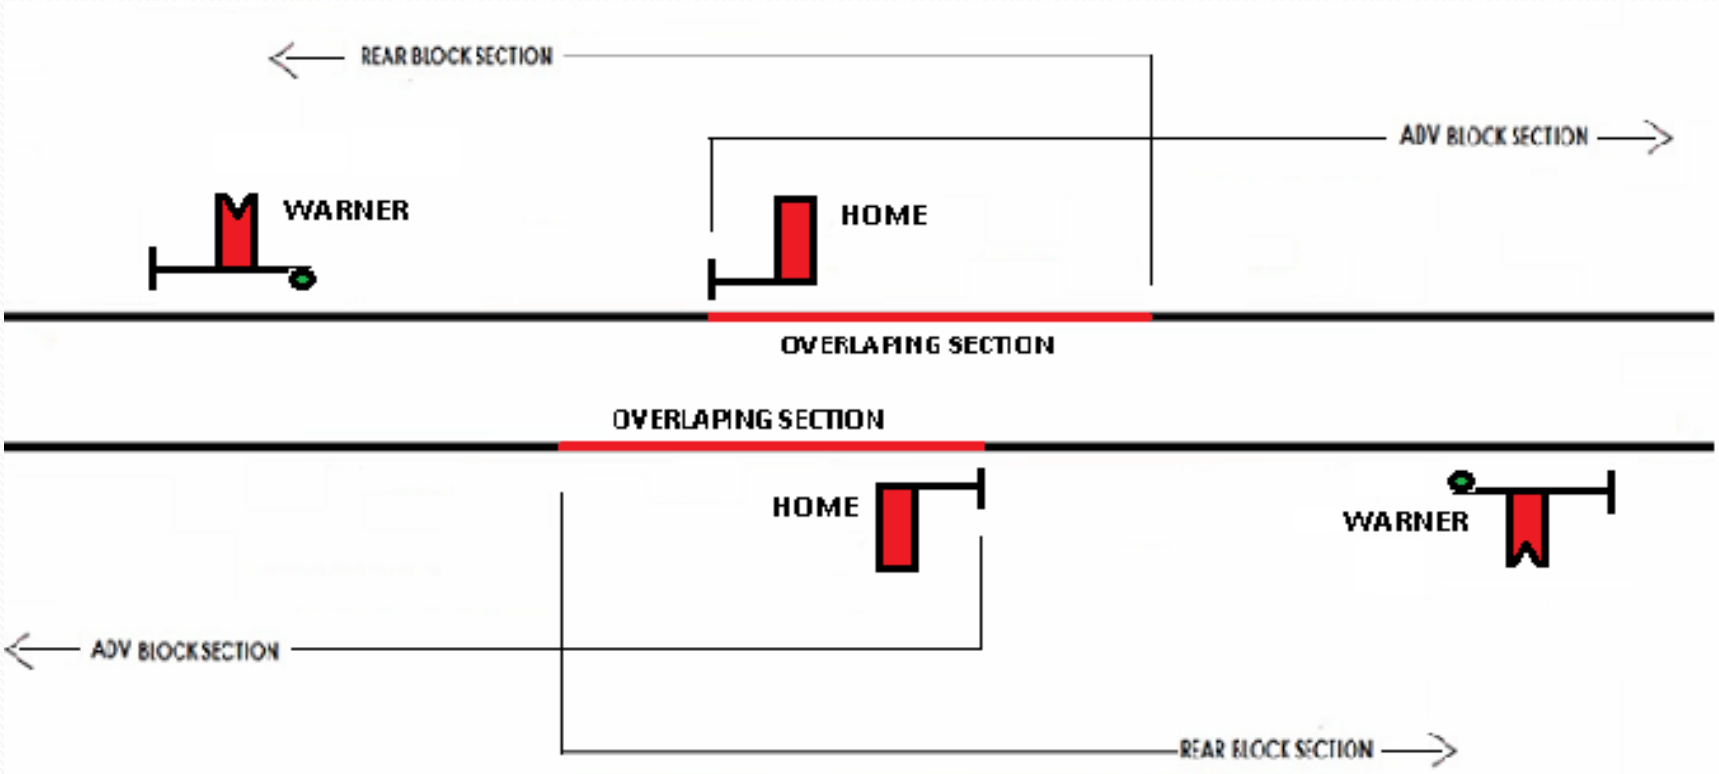


CLASS 'C' DOUBLE LINE STATION IN TWO ASPECT SIGNALS WITH WARNER AND HOME SIGNALS

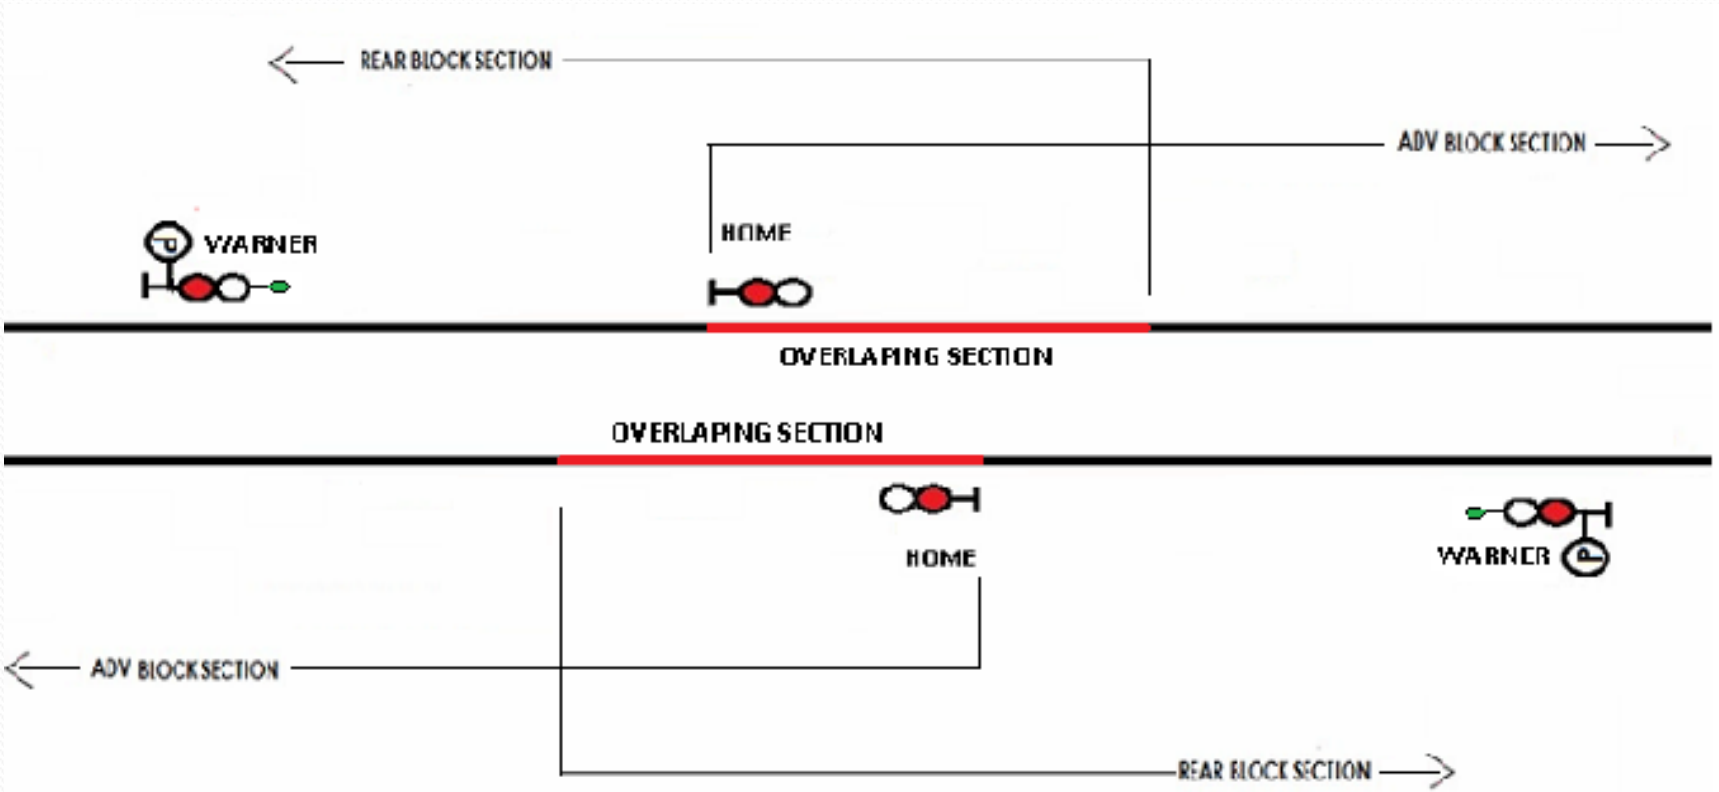

CLASS 'C' DOUBLE LINE STATION IN MULTIPLE ASPECT SIGNALS WITH DISTANT AND HOME SIGNALS

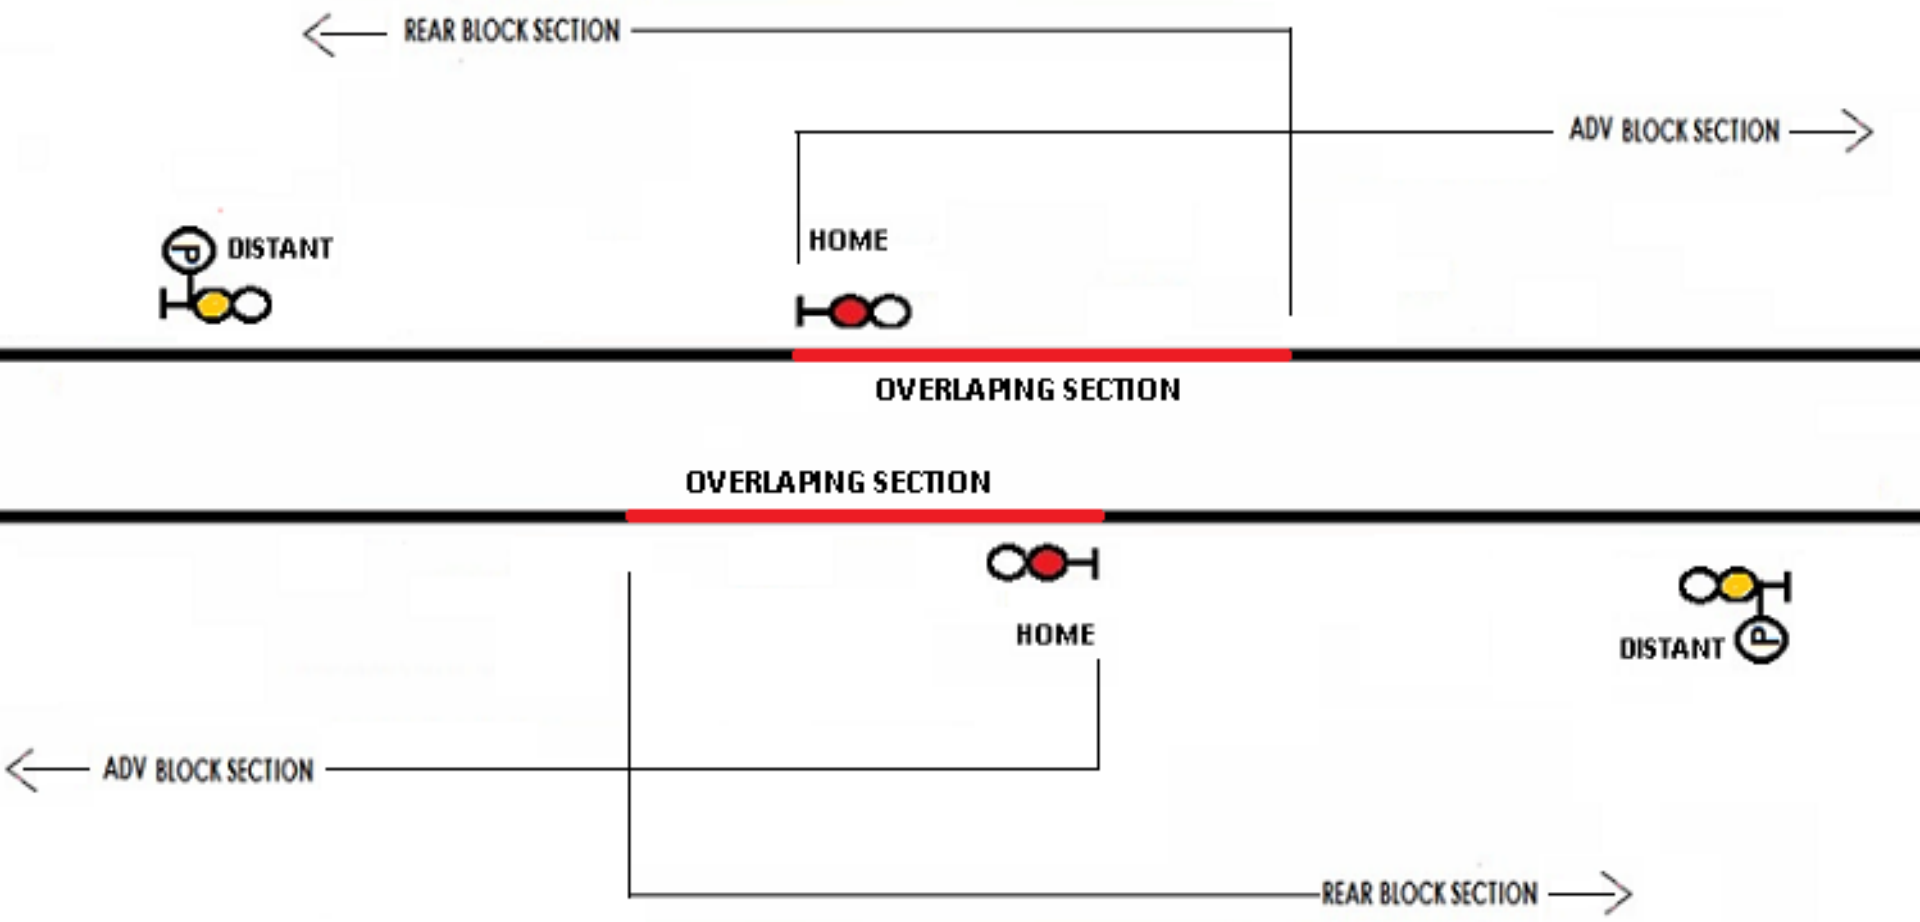

CLASS 'C' DOUBLE LINE STATION IN MULTIPLE ASPECT SIGNALS WITH DISTANT , HOME & STARTER SIGNALS

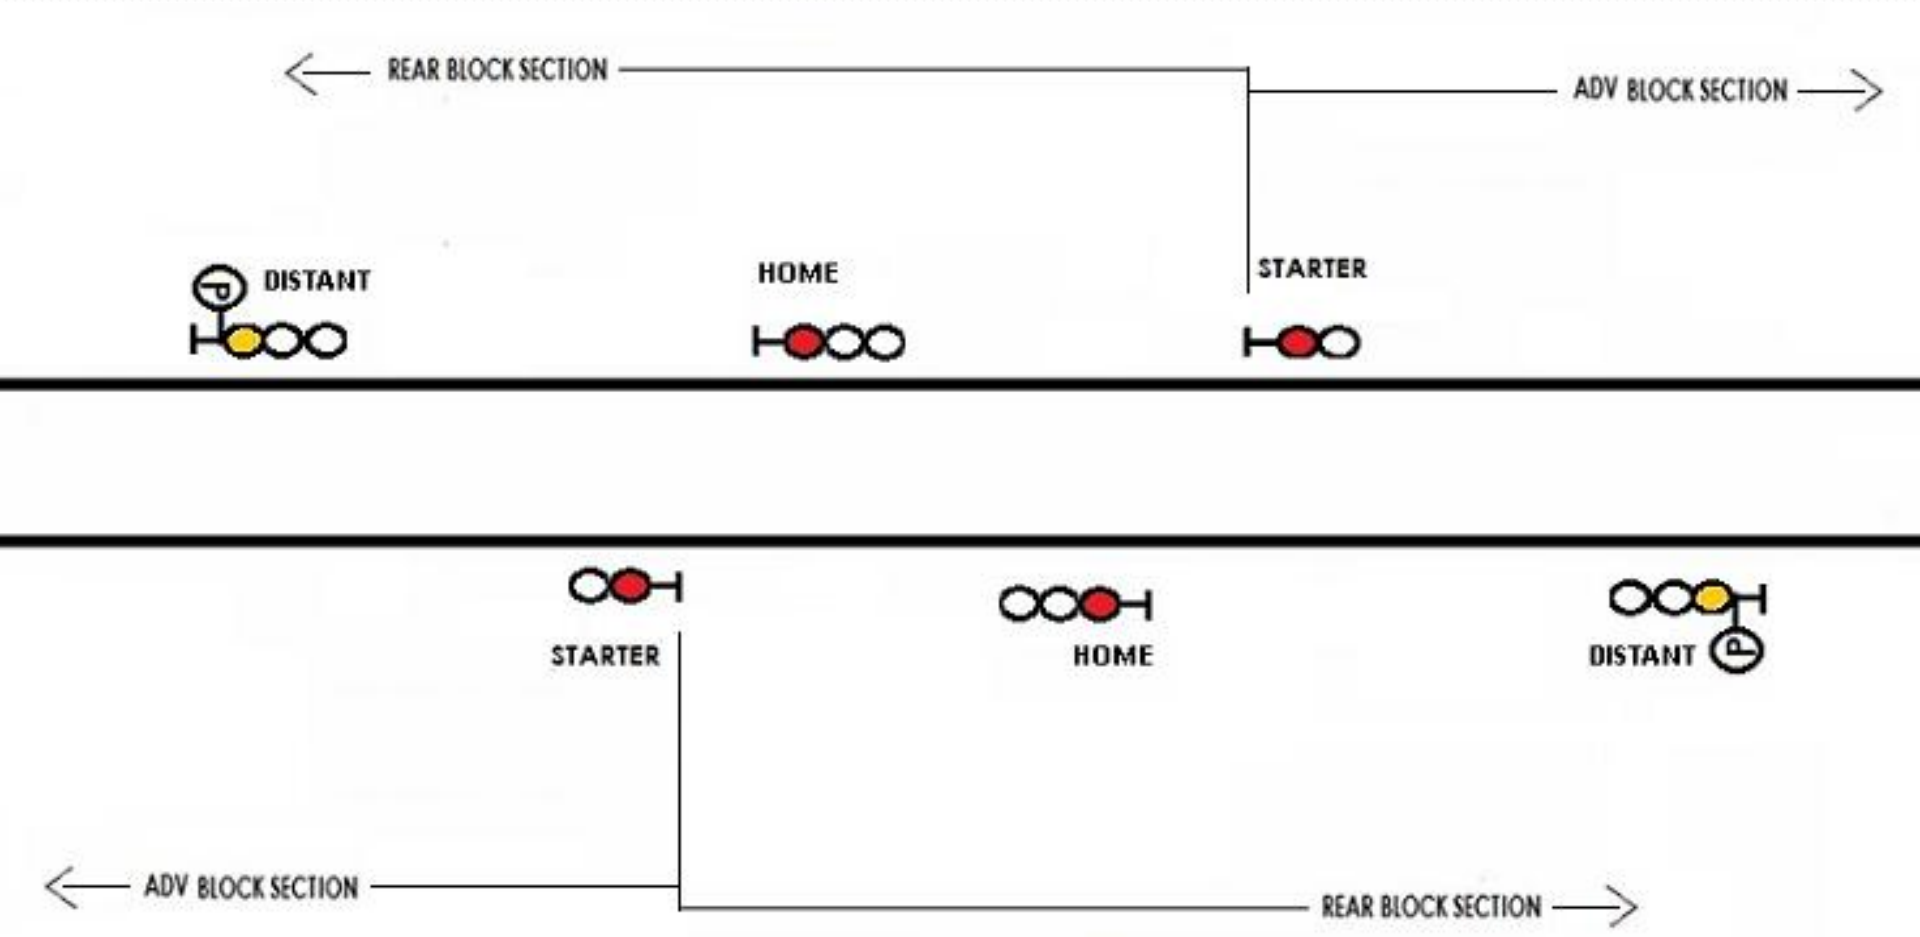

EQUIPMENTS OF SIGNALS

STATION	MINIMUM SIGNALS	MAXIMUM SIGNALS
"A" CLASS STATION	WARNER , HOME, STARTER.	WARNER, HOME, STARTER, ADV. STR,
"B" CLASS SINGLE LINE T/A	OUTER & HOME.	OUTER, WARNER, HOME, STR.& ADV. STR.
"B" CLASS DOUBLE LINE T/A	OUTER , HOME & STR.	OUTER, WARNER, HOME, STR.& ADV. STR.
"B" CLASS SINGLE LINE M/A	DISTANT , HOME & STR.	DISTANT , HOME, STR.& ADV. STR.
"B" CLASS DOUBLE LINE M/A	DISTANT , HOME & STR.	DISTANT , HOME, STR.& ADV. STR.
"C" CLASS T/A	WARNER , HOME	WARNER , HOME
"C" CLASS M/A	DISTANT , HOME	DISTANT , HOME

CLASS "D" STATION

- Class 'D' stations are stopping places which are situated between two consecutive block stations, and do not form the boundary of any block section.

"DK" CLASS STATION

- Those D class stations at which there is out – lying siding are termed as 'DK' stations.

Special class station

- Any station which cannot be worked solely under 'A', 'B', 'C' or 'D' class conditions, is termed as 'Special class.
- E.g.- All station in automatic block section.

THANKYOU

Dhananjay Kumar Singh
Instructor Transportation
ZRTI/ Bhuli